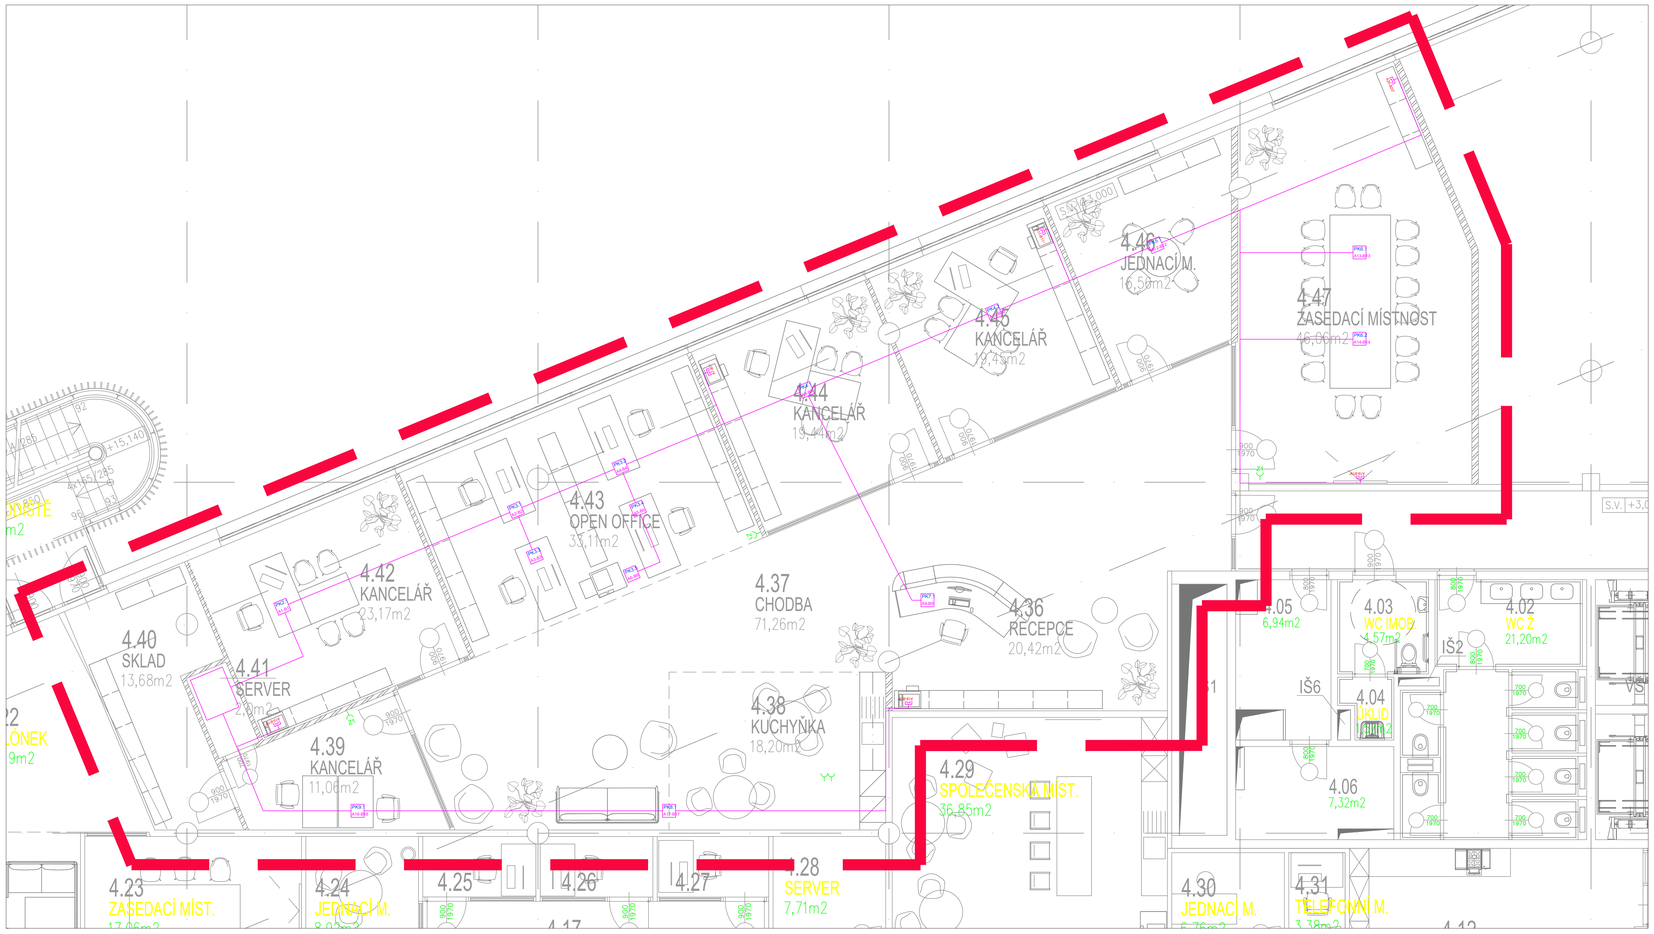

LEGENDA MÍSTNOSTÍ:

Č.M.	NÁZEV MÍSTNOSTI	PLOCHA [m2]	PODLAHA	SVĚTLÁ VÝŠKA	STROP	POZNÁMKA
4.01	CHODBA	77,46		3,00		OBKLAD
4.02	WC ŽENY	21,20		3,00		OBKLAD
4.03	WC IMOBILNÍ	4,57		3,00		OBKLAD
4.04	ÚKLID	1,57		3,00		OBKLAD
4.05	-	6,94		3,00		
4.06	-	7,32		3,00		
4.07	WC MUŽI	20,68		3,00		OBKLAD
4.08	SCHODIŠTĚ	16,88		3,00		
4.09	HALA 1	320,10		3,00		
4.10	TERASA	14,49		3,00		
4.11	SCHODIŠTĚ	19,05		3,00		
4.12	COFFE BAR	31,81	VINYL	3,00	PEVNÝ SDK PODHLED	
4.13	ZASEDACÍ MÍSTNOST	31,79	KOBEREC	3,00	KAZETOVÝ PODHLED	
4.14	TELEFONNÍ MÍSTNOST	3,44	KOBEREC	3,00	KAZETOVÝ PODHLED	
4.15	JEDNACÍ MÍSTNOST	8,67	KOBEREC	3,00	KAZETOVÝ PODHLED	
4.16	OPEN SPACE	46,52	KOBEREC	3,00	PEVNÝ SDK PODHLED KAZETOVÝ PODHLED	
4.17	KORIDOR	67,98	DLAŽBA	3,00	PEVNÝ SDK PODHLED	
4.18	TELEFONNÍ MÍSTNOST	3,53	KOBEREC	3,00	KAZETOVÝ PODHLED	
4.19	TELEFONNÍ MÍSTNOST	3,52	KOBEREC	3,00	KAZETOVÝ PODHLED	
4.20	JEDNACÍ MÍSTNOST	7,25	KOBEREC	3,00	KAZETOVÝ PODHLED	
4.21	OPEN SPACE	104,53	KOBEREC	3,00	PEVNÝ SDK PODHLED KAZETOVÝ PODHLED	
4.22	SALÓNEK	29,19	KOBEREC	3,00	PEVNÝ SDK PODHLED KAZETOVÝ PODHLED	
4.23	ZASEDACÍ MÍSTNOST	17,06	KOBEREC	3,00	KAZETOVÝ PODHLED	
4.24	JEDNACÍ MÍSTNOST	8,92	KOBEREC	3,00	KAZETOVÝ PODHLED	
4.25	TELEFONNÍ MÍSTNOST	3,62	KOBEREC	3,00	KAZETOVÝ PODHLED	
4.26	TELEFONNÍ MÍSTNOST	3,61	KOBEREC	3,00	KAZETOVÝ PODHLED	
4.27	TELEFONNÍ MÍSTNOST	3,60	KOBEREC	3,00	KAZETOVÝ PODHLED	
4.28	SERVER	7,71	ANTISTATICKÉ PVC	3,00	KAZETOVÝ PODHLED	
4.29	SPOLEČENSKÁ MÍSTNOST	36,85	VINYL	3,00	PEVNÝ SDK PODHLED KAZETOVÝ PODHLED	
4.30	JEDNACÍ MÍSTNOST	6,76	KOBEREC	3,00	KAZETOVÝ PODHLED	
4.31	TELEFONNÍ MÍSTNOST	3,38	KOBEREC	3,00	KAZETOVÝ PODHLED	
4.32	HALA 2	567,15	KOBEREC	3,00	KAZETOVÝ PODHLED	
4.33	SKLAD	15,15	KOBEREC	3,00	KAZETOVÝ PODHLED	
4.34	SKLAD	12,91	KOBEREC	3,00	KAZETOVÝ PODHLED	
4.35	SERVER	9,44	ANTISTATICKÉ PVC	3,00	KAZETOVÝ PODHLED	
4.36	RECEPCE	20,42	KOBEREC ČTVERCE 500x500	3,00	KAZETOVÝ PODHLED	
4.37	CHODBA	71,26	KOBEREC ČTVERCE 500x500	3,00	KAZETOVÝ PODHLED	
4.38	KUCHYŇKA	18,20	PVC	3,00	KAZETOVÝ PODHLED	
4.39	KANCELÁŘ	11,06	KOBEREC ČTVERCE 500x500	3,00	KAZETOVÝ PODHLED	
4.40	SKLAD	13,68	KOBEREC ČTVERCE 500x500	3,00	KAZETOVÝ PODHLED	
4.41	SERVER	2,00	ANTISTATICKÉ PVC	3,00	KAZETOVÝ PODHLED	
4.42	KANCELÁŘ	23,17	KOBEREC ČTVERCE 500x500	3,00	KAZETOVÝ PODHLED	
4.43	OPEN OFFICE	33,11	KOBEREC ČTVERCE 500x500	3,00	KAZETOVÝ PODHLED	
4.44	KANCELÁŘ	19,44	KOBEREC ČTVERCE 500x500	3,00	KAZETOVÝ PODHLED	
4.45	KANCELÁŘ	19,45	KOBEREC ČTVERCE 500x500	3,00	KAZETOVÝ PODHLED	
4.46	JEDNACÍ MÍSTNOST	16,56	KOBEREC ČTVERCE 500x500	3,00	KAZETOVÝ PODHLED	
4.47	ZASEDACÍ MÍSTNOST	46,06	KOBEREC ČTVERCE 500x500	3,00	KAZETOVÝ PODHLED	

Datové rozvody

Zásuvkové obvody

Světelné obvody

LAN zásuvka (* znamená že se zásuvka nachází ve 120cm)

1f zásuvka

1f zásuvka venkovní

3N — 3f zásuvka

1f zásuvka (dvojzásuvka)

PK1 A1-B1 — Podlahová skříň

Ethernetová zásuvka

LEGENDA:

- STÁVAJÍCÍ KONSTRUKCE
- NAVRHOVANÉ SDK KONSTRUKCE TL. 150; 100 MM
- NAVRHOVANÉ PROSKLENÉ PŘÍČKY
- ŘEŠENÝ PROSTOR

Výpis platných norem ČSN

Nap. soustava: TN-C-S, 3 +(PEN) PE +N, 400V/230V, 50 Hz stř.

ČSN 332000-4-41 - ed.3 - (8/2007) + Z1 (4/2010):

- živých částí - Všeobecně dle čl. 412.1
- dle čl. 413.1
- ČSN 332000-5-51 ed.3
- ČSN 332000-5-52 ed.2
- ČSN 332000-5-534 ed.2
- ČSN 332000-4-41 - ed.3 - (01/2018)
- ČSN 332000-4-42- ed.2
- ČSN 332000-4-43 - ed.3
- ČSN 332000-4-444
- ČSN 332000-4-46 - ed.3
- ČSN 332000-7-701 ed.2
- ČSN 332000-7-704 ed.3
- ČSN EN 50174-2 ed.2
- ČSN 332130 ed.3 (12/2014)
- ČSN 33-2000-6 ed.2 (03/2017)
- Veškeré zásuvky obsluhované nepoučenými osobami dle normy ČSN 33-2000-4-41 ed. 3 budou připojeny přes proudový chránič 30mA.

Nap. soustava: TN-C-S, 3 +(PEN) PE +N, 400V/230V, 50 Hz stř.
Ochrana proti dotyku: dle ČSN 33-2000-4-41 ed.3
samočinným odpojením od zdroje
pospojením
proudovými chrániči
Prostředí: dle ČSN 33-2000-5-51 ed.3

VOŠ A SPŠ Elektrotechnická F. Křižíka	HIP:	ZODPOV. PROJEKTANT:	VYPRACOVAL:	SPEC.:
				STUPEŇ: DPS
				Č.ZAK.: 01
voš a spšelektro PŘÍKOPY	INVESTOR: VOŠ a SPŠE Františka Křižíka			DATUM:
	MÍSTO ST.:			
	AKCE: Kancelářské prostory			FORMÁT: A0
	OBJEKT: Kanceláře			MĚŘÍTKO: 1:50
	VÝKRES: Optická kabeláž v kancelářích			Č.VÝKR.: 01

Dokumentace je chráněna autorským právem a nesmí se rozmnožovat a poskytovat třetím osobám bez souhlasu autorů nebo investora